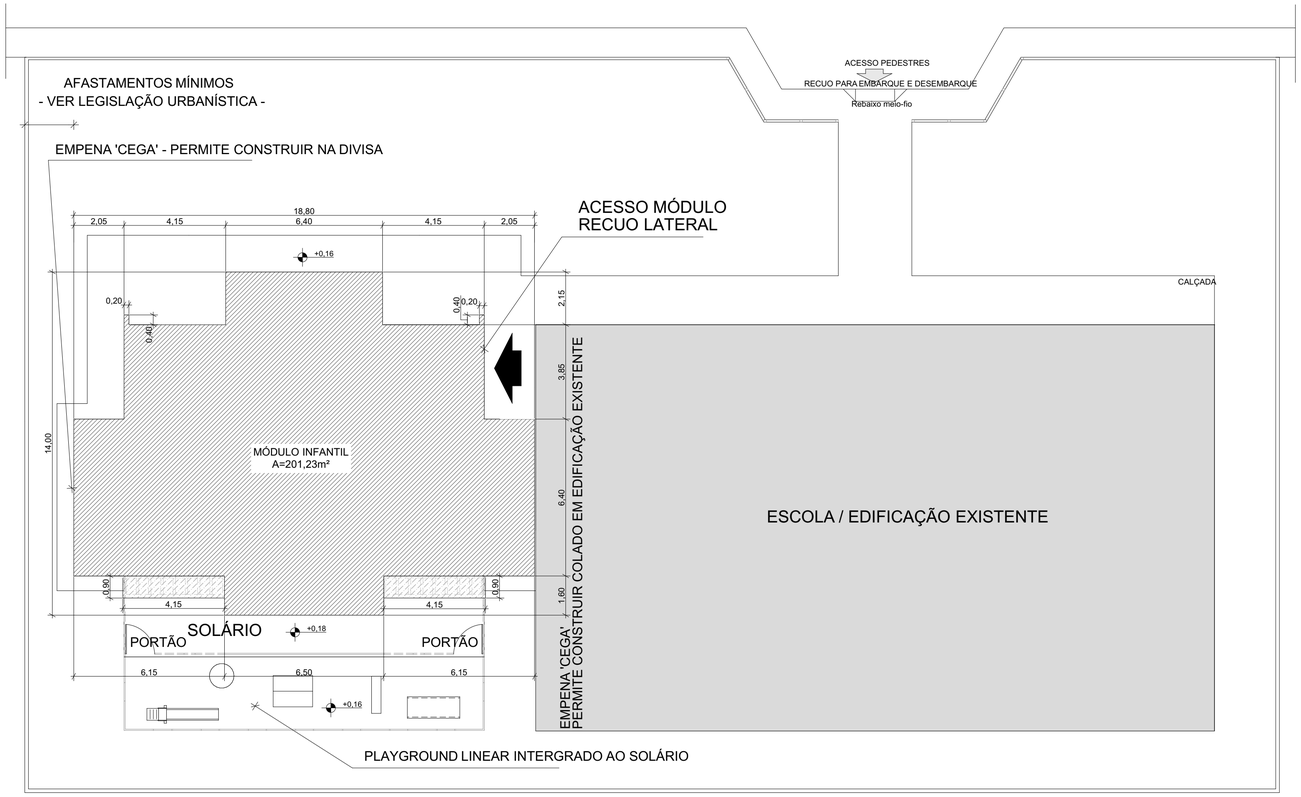


1 IMPLANTAÇÃO HIPOTÉTICA 01
ESCALA1:125

- MÓDULO INFANTIL 'COLADO' NA EDIFICAÇÃO EXISTENTE E, OU NA DIVISA.
- SOLÁRIO INTEGRADO AO 'PLAYGROUND'

NOTAS GERAIS:

- O MÓDULO DE EDUCAÇÃO INFANTIL DEVE SER IMPLANTADO COMO COMPLEMENTAR NAS ESCOLAS EXISTENTES:
  A. ATENDENDO A DEMANDA DE EDUCAÇÃO INFANTIL (PRÉ-ESCOLA) JUNTO AO ENSINO FUNDAMENTAL,
  B. OU AMPLIANDO O ATENDIMENTO DE ESCOLAS EXISTENTES DE EDUCAÇÃO INFANTIL.
- AS ÁREAS ADMINISTRATIVAS E DE SERVIÇO SERÃO ATENDIDAS PELA ESCOLA EXISTENTE. O MÓDULO DE EDUCAÇÃO INFANTIL PREVÊ APENAS APOIO A ÁREA DE REFEITÓRIO.
- AS IMPLANTAÇÕES HIPOTÉTICAS SERVEM APENAS COMO EXEMPLO, VISTO QUE O PROJETO DO MÓDULO DE EDUCAÇÃO INFANTIL NÃO POSSUI TERRENO PADRÃO E SERÁ IMPLANTADO JUNTO A EDIFICAÇÕES ESCOLARES EXISTENTES.
- O PROJETO DO MÓDULO DE EDUCAÇÃO INFANTIL PREVÊ EMPENAS 'CEGAS' QUE PERMITEM A CONSTRUÇÃO TANTO NA DIVISA QUANTO COLADA EM EDIFICAÇÃO EXISTENTE.
- OS ACESSOS PREVISTOS NO PROJETO PODEM SER ESPELHADOS, OCORREM DA MESMA FORMA NA ESQUERDA OU NA DIREITA CONFORME ORIENTAÇÃO DO DESENHO.
- AS MELHORES ORIENTAÇÕES DO SOLÁRIO SÃO NORTE E LESTE - VER MEMORIAL DESCRITIVO.
- OS ITENS DE IMPLANTAÇÃO, TAIS COMO: JARDINS, CALÇADAS E PLAYGROUND E ETC, **NÃO** FAZEM PARTE DO MÓDULO DE EDUCAÇÃO INFANTIL.

NOTAS

- MEDIDAS E NÍVEIS EM METROS;
- VERIFICAR POSIÇÃO EXATA DOS PILARES NO PROJETO ESTRUTURAL;
- VERIFICAR DETALHES CONSTRUTIVOS PERTINENTES NAS PRANCHAS DE DETALHAMENTO;
- EM CASO DE CONFLITO DE INFORMAÇÕES ENTRE O PROJETO GRÁFICO E O MEMORIAL DESCRITIVO, PREVALECE A INFORMAÇÃO CONTIDA NOS DESENHOS;
- ALTERAÇÕES NESTE PROJETO SOMENTE COM AUTORIZAÇÃO EXPRESSA DO FNDE

REFERENCIAS:


- PLANILHA DE QUANTITATIVOS
- MEMORIAL DESCRITIVO E ESPECIFICAÇÕES TÉCNICAS

LEGENDA			
+0,00 (NA) +0,00 (NO) / +0,03 (NA)	INDICAÇÃO NÍVEIS PLANTA E CORTE	01	INDICAÇÃO DE VISTAS
X PE-XX	INDICAÇÃO DE CORTES	P1	ESPECIFICAÇÃO DE MATERIAIS DE PISO
X PE-XX	INDICAÇÃO DE FACHADAS	I1 E1	ESPECIFICAÇÃO DE MATERIAIS DE PAREDE INTERNA E EXTERNA
PMX JA-X	INDICAÇÃO DE PORTAS E JANELAS	T1	ESPECIFICAÇÃO DE MATERIAIS DE TETO
DET X XX	INDICAÇÃO DE DETALHES		

QUADRO DE ÁREAS

ÁREAS EDIFICADAS			
BLOCO	ÁREA CONSTRUÍDA	ÁREA ABERTA COBERTA	ÁREA TOTAL
MÓDULO INFANTIL	201,23	7,47	208,70
TOTAL ÁREA	201,23 m²	7,47 m²	208,70 m²

ÁREAS NÃO EDIFICADAS	
ÁREAS EXTERNAS	ÁREA
IMPERMEÁVEL	106,53
PERMEÁVEL	44,10
TOTAL ÁREA EXTERNA	150,63 m²

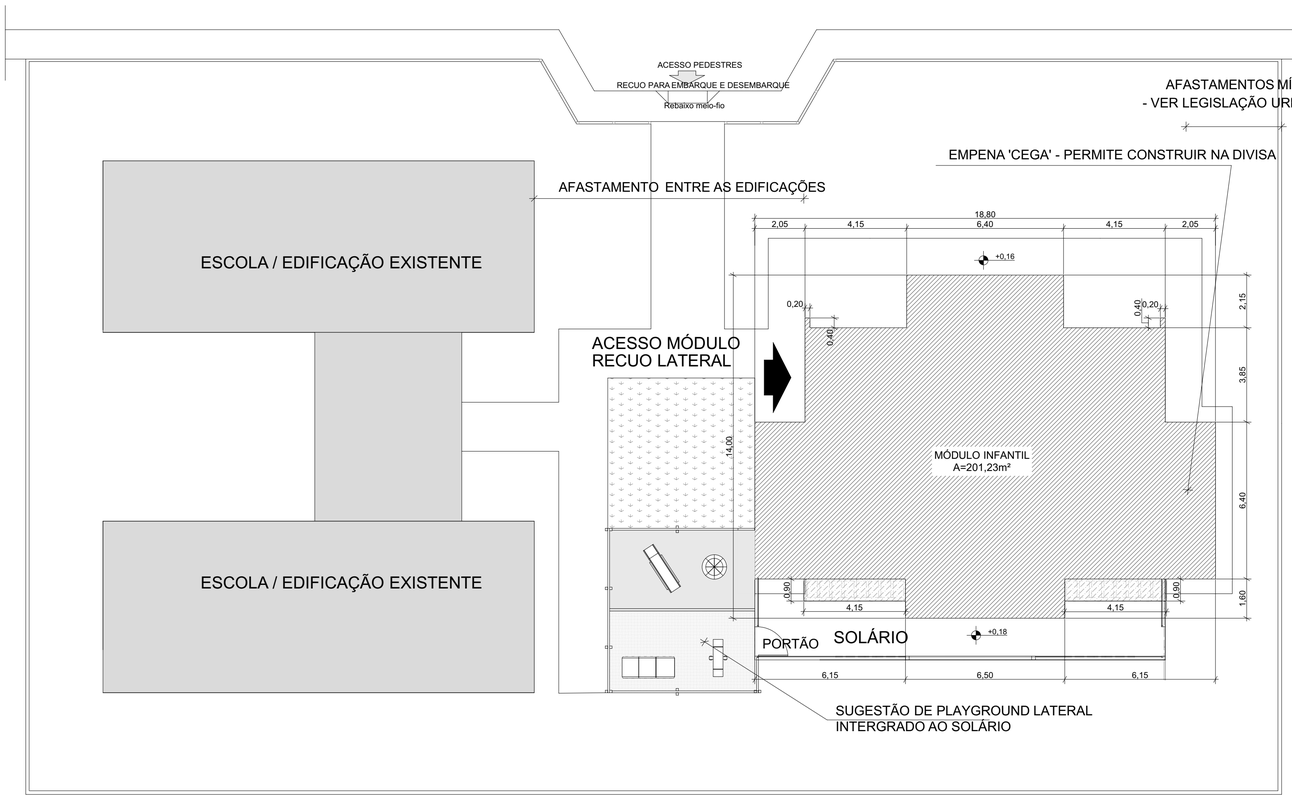

2 IMPLANTAÇÃO HIPOTÉTICA 02
ESCALA1:125

- MÓDULO INFANTIL AFASTADO DA EDIFICAÇÃO EXISTENTE.
- SOLÁRIO INTEGRADO AO 'PLAYGROUND' LOCALIZADO NAS LATERAIS.

IMPORTANTE:

1. AS IMPLANTAÇÕES DEVEM ATENDER A LEGISLAÇÃO URBANÍSTICA MUNICIPAL (ÍNDICE DE APROVEITAMENTO, TAXA DE OCUPAÇÃO, AFASTAMENTOS MÍNIMOS E ETC).
2. DEVEM SER OBSERVADAS A LEGISLAÇÃO DE COMBATE E PROTEÇÃO CONTRA INCÊNDIO ESTADUAIS, ANALISADAS EM CONJUNTO COM A ESCOLA EXISTENTE (ROTAS DE FUGA, INSTALAÇÕES DE GÁS E ETC).
3. DEVEM SER ATENDIDAS AS NORMAS DA VIGILÂNCIA SANITÁRIA RELATIVAS A SAÚDE E HIGIENE DAS ÁREAS DE ALIMENTAÇÃO: REFEITÓRIOS E COZINHAS EXISTENTES EM CONJUNTO COM O APOIO DO MÓDULO INFANTIL.
4. AS INSTALAÇÕES COMPLEMENTARES (HIDRÁULICA, ELÉTRICA E ETC) REPRESENTAM UM AMENTOU DE DEMANDA COM RELAÇÃO A ESCOLA EXISTENTE E AS SOLUÇÕES TÉCNICAS DEVEM SER ESTUDADAS NA IMPLANTAÇÃO.

Nº	DATA	DESCRIÇÃO
01	JANEIRO/ 2025	Revisão do Projeto Arquitetônico Módulo Infantil Modelo Padrão FNDE em metodologia Building Information Modeling. Alteração para atender a NBR 9050/2020; Aumento da dimensão do módulo para atender alterações de layout dos ambientes copa e instalações sanitárias.

CONTROLE DE REVISÕES

fnde MINISTÉRIO DA EDUCAÇÃO

PROJETO PADRÃO - FNDE

PROPRIETÁRIO:

ENDEREÇO:

MUNICÍPIO - UF:

PROPRIETÁRIO:

RESP. TÉCNICO: CAU / CREA

AUTOR DO PROJETO: CAU / CREA

APROVAÇÕES

CAU / CREA

PREFEITURA / RA

OBSERVAÇÕES:

MÓDULO DE EDUCAÇÃO INFANTIL

PROJETO DE ARQUITETURA

COORDENAÇÃO			
CGEST - Coordenação Geral de Infraestrutura Educacional	IMPLANTAÇÃO		ARQ
FORMATO (841x594)	REVISÃO R.00 R.01	ESCALA 1:125	PRANCHA 01/18
		DATA EMISSÃO JANEIRO/2025	